




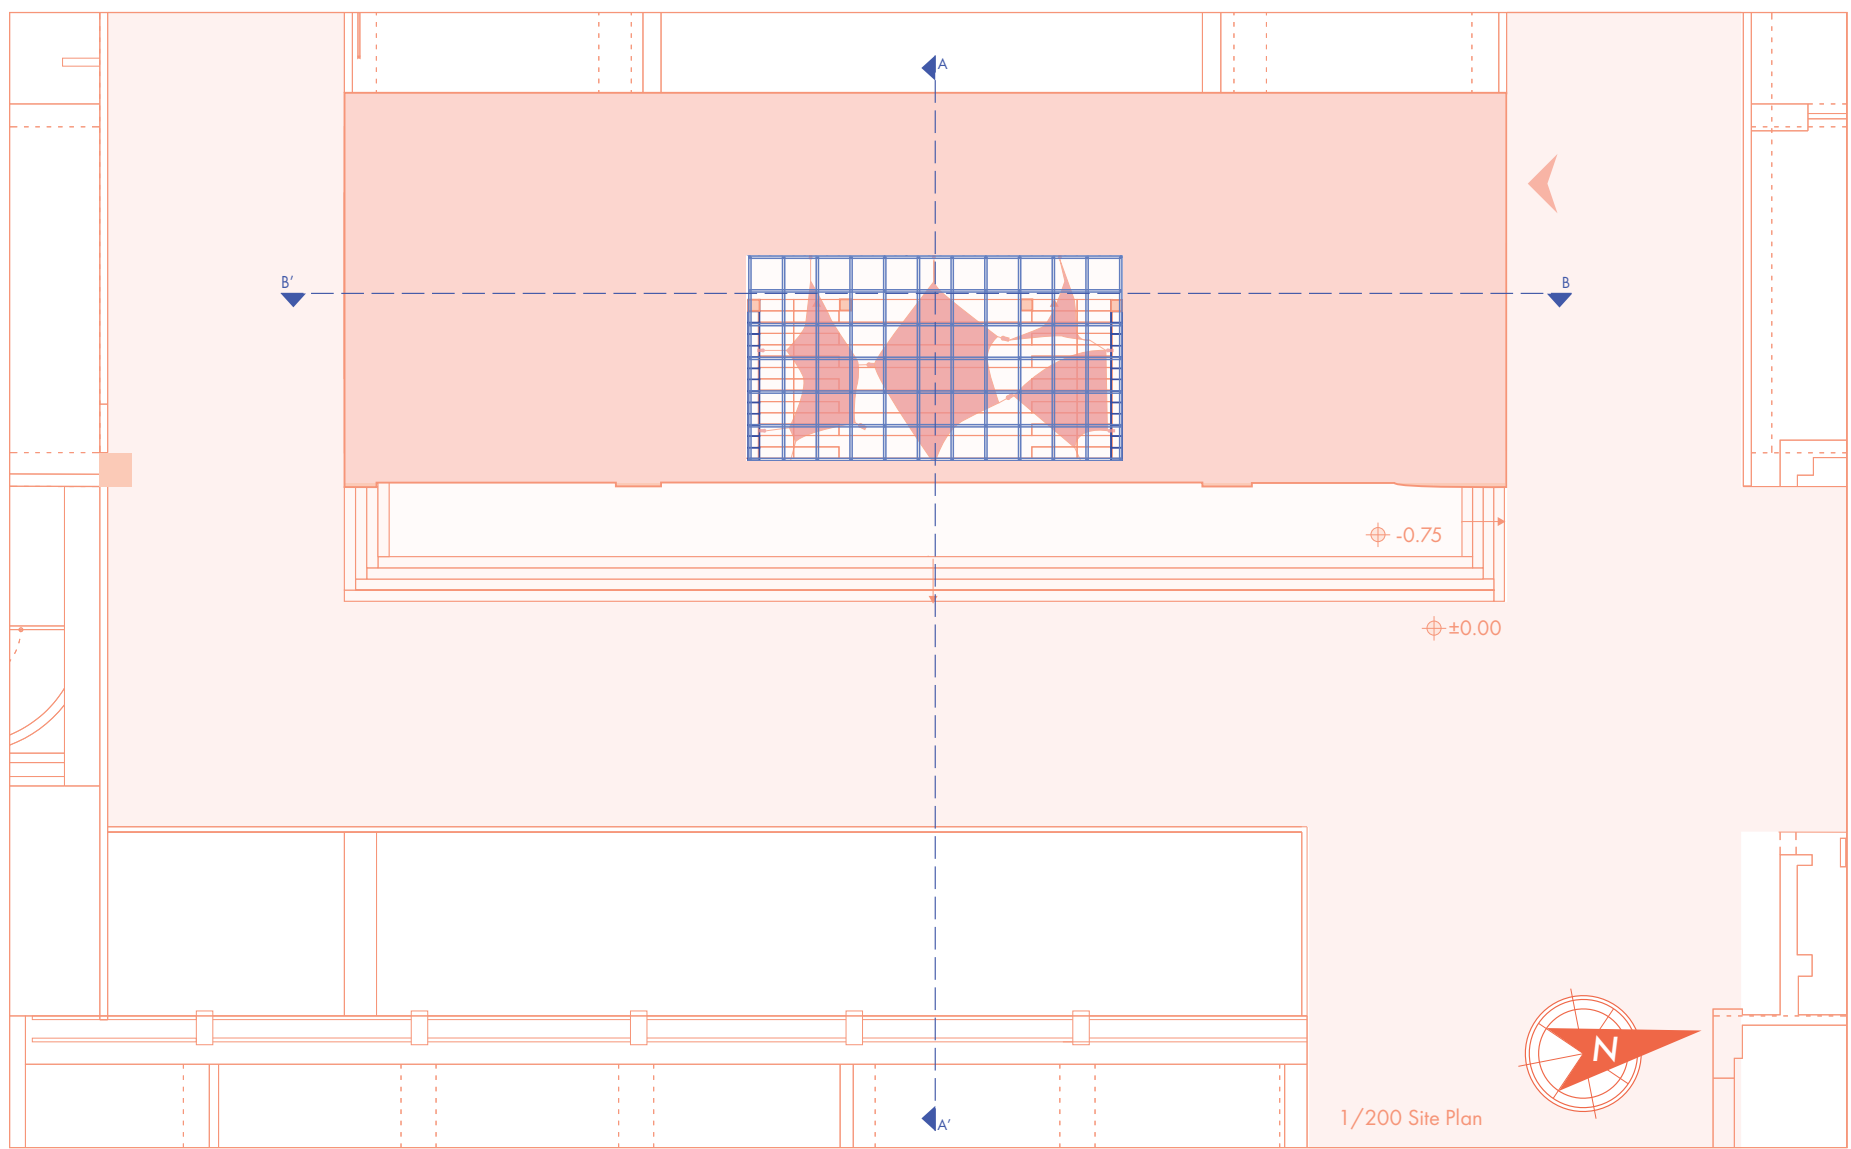


The space is never finished — it is **always in progress**. Bioplastics decay slowly, and as they do, their texture hardens, their colors darken, and they lose transparency. These changes also shift the quality of light and shadow in the space. Sometimes they look like stained jelly under light. As materials rot, they are replaced with new ones, so **the structure is constantly rebuilding itself**, shaped by time, light, and decay.



This cycle of decay and renewal is **not hidden** — it becomes **the identity of the space**. Visitors can see the aging materials, touch them, and even leave marks that change their surface. These reactions—triggered by light, touch, and time—become part of the archive itself. The structure does **not aim to preserve perfection, but to document transformation**. Each layer, each patch added to repair the old ones, carries traces of human presence and environmental conditions. In this way, **the archive becomes a living record of disappearance and change**.

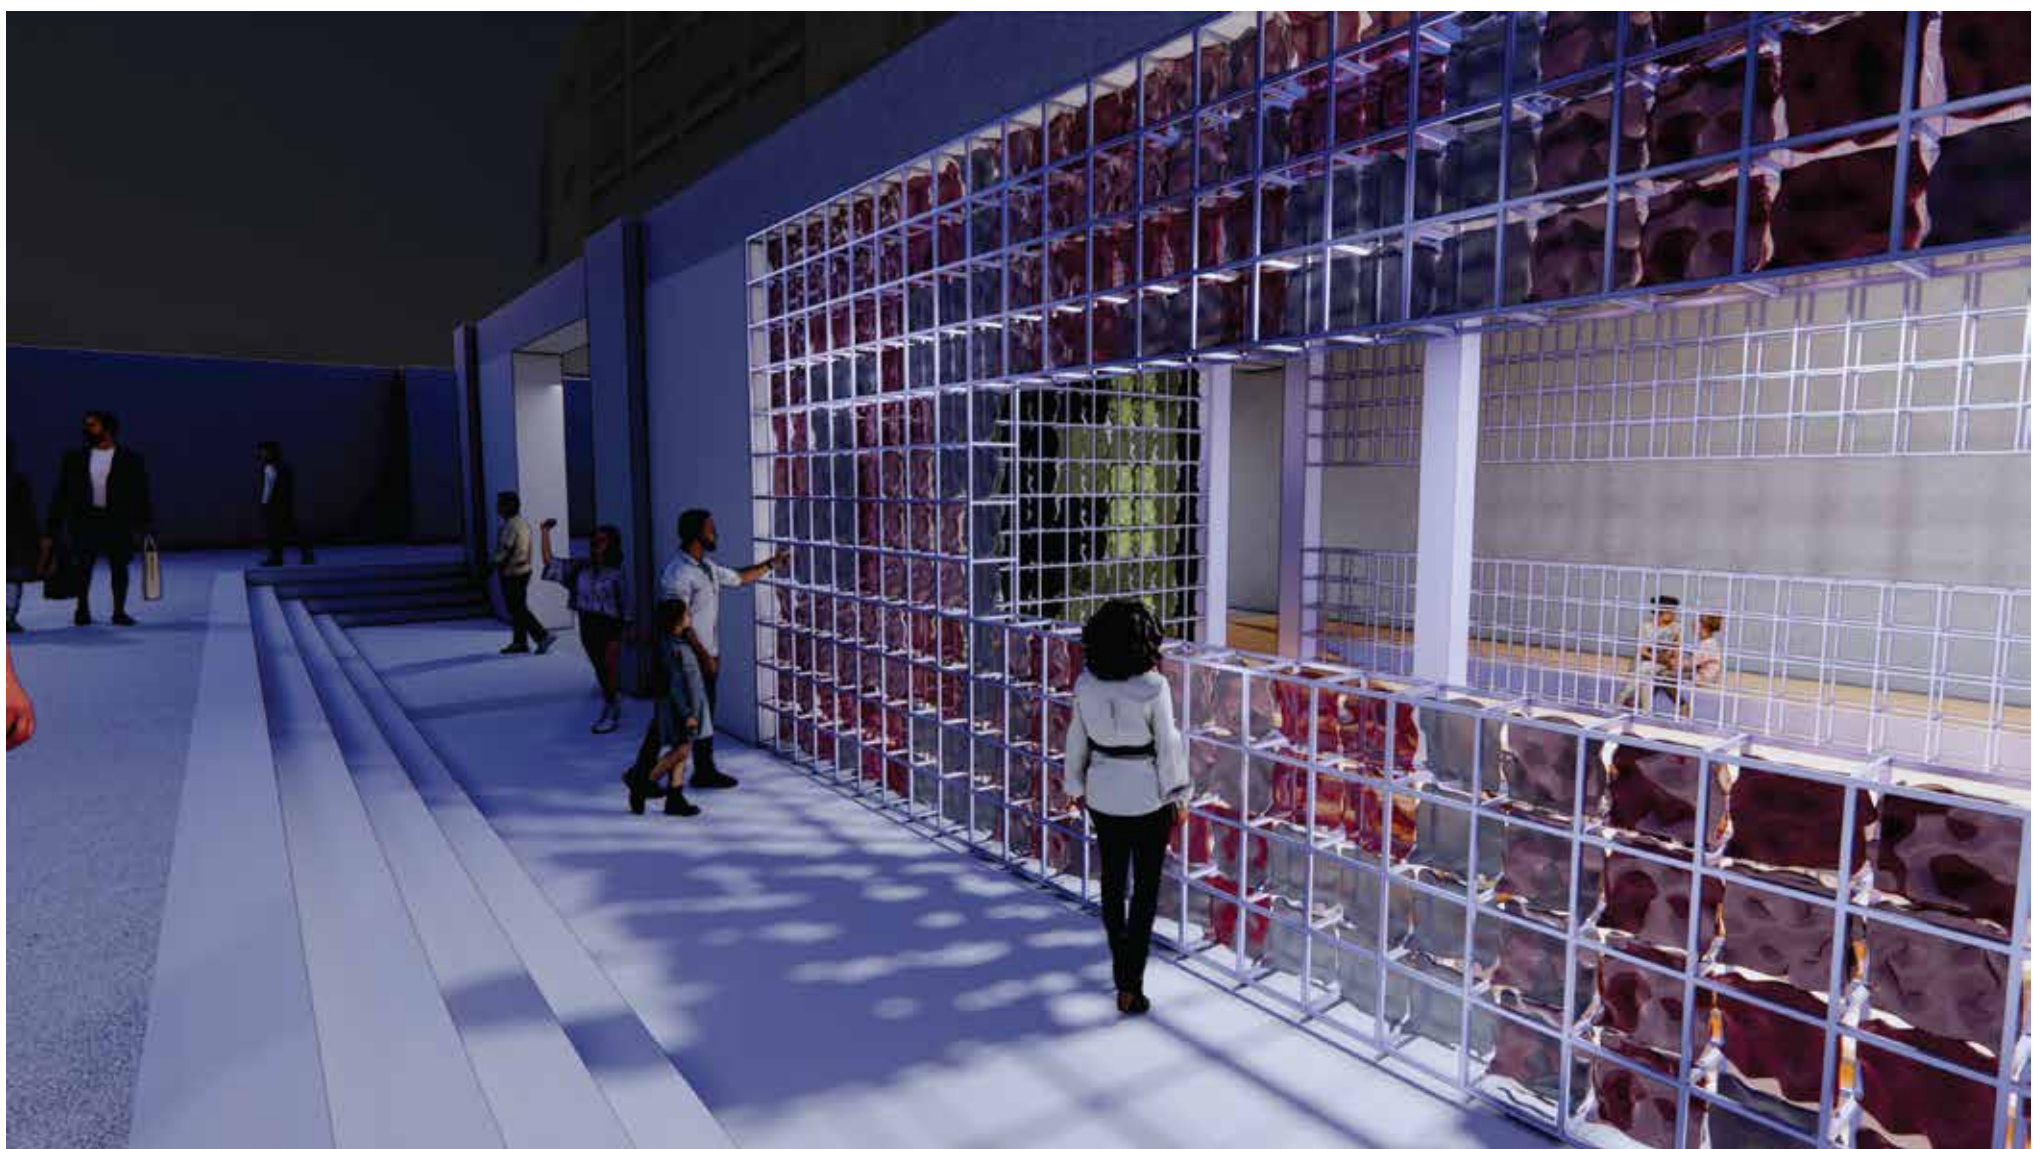


Facade View

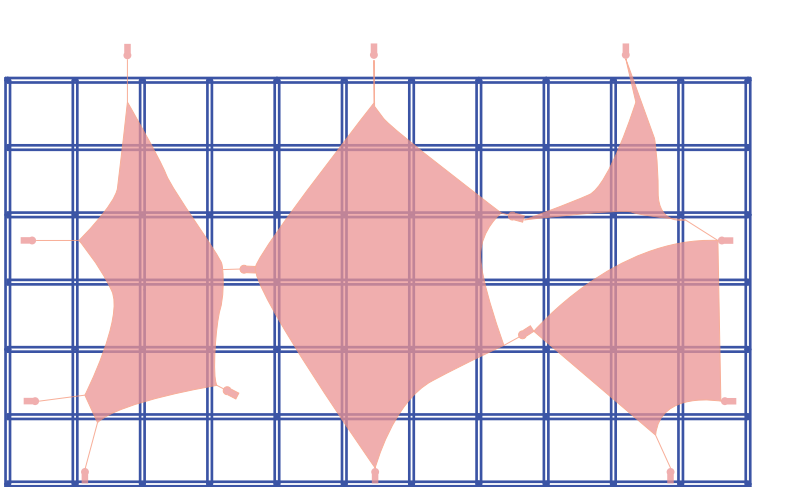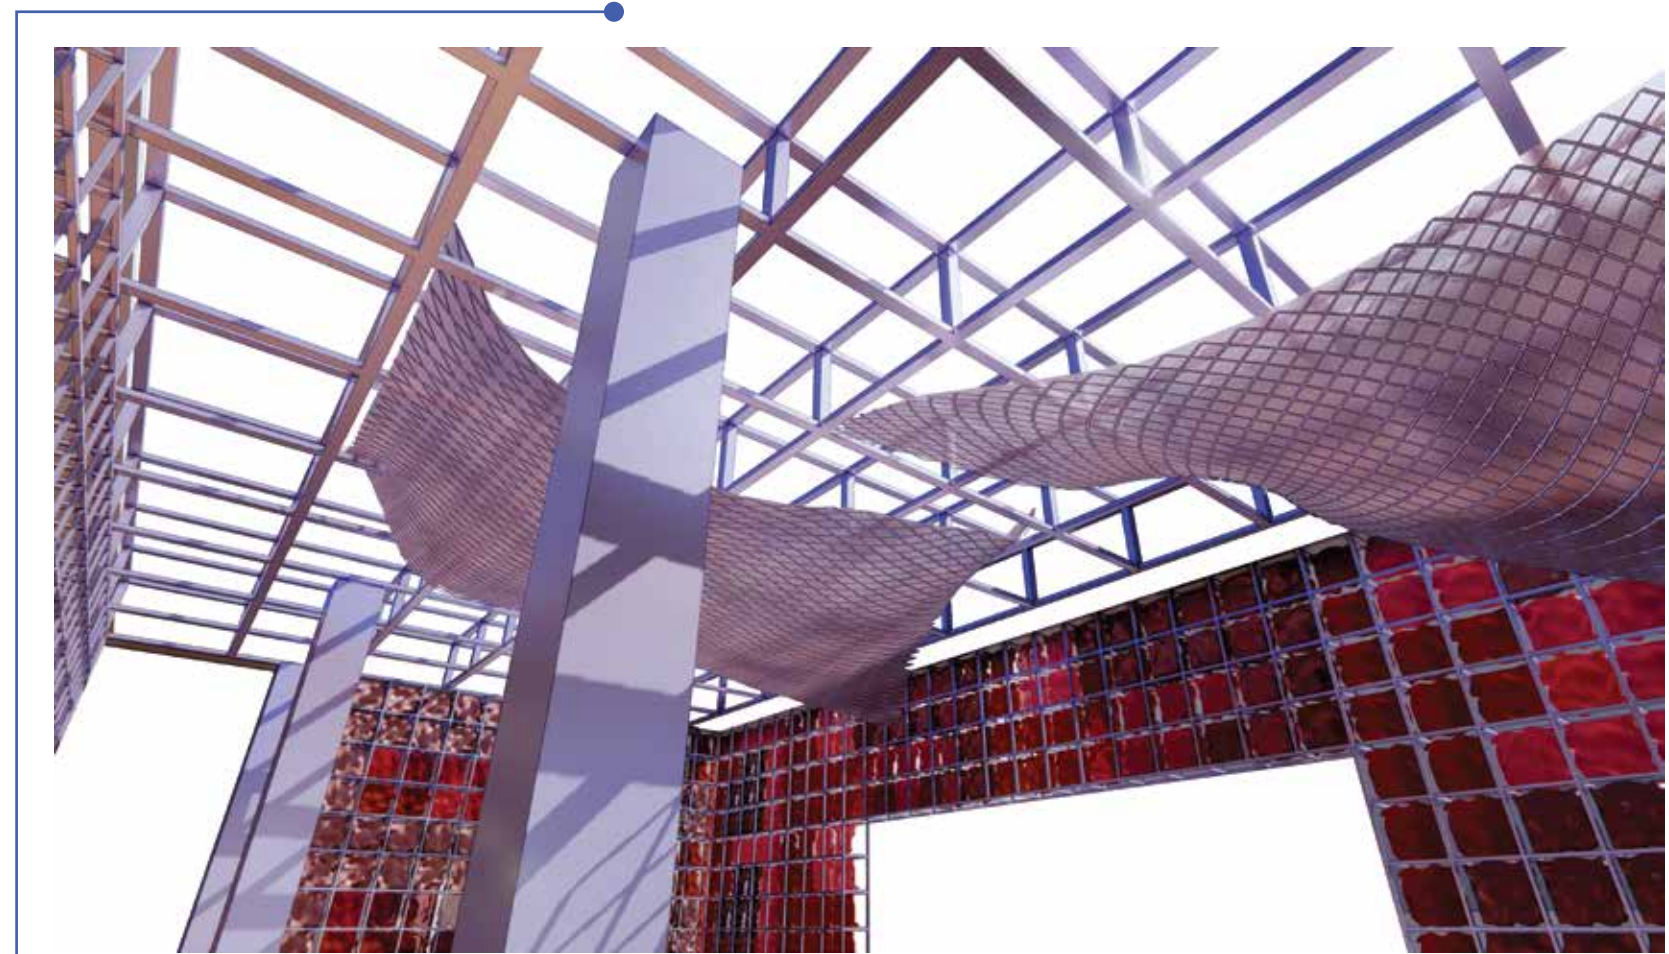

1/100 Ceiling Plan

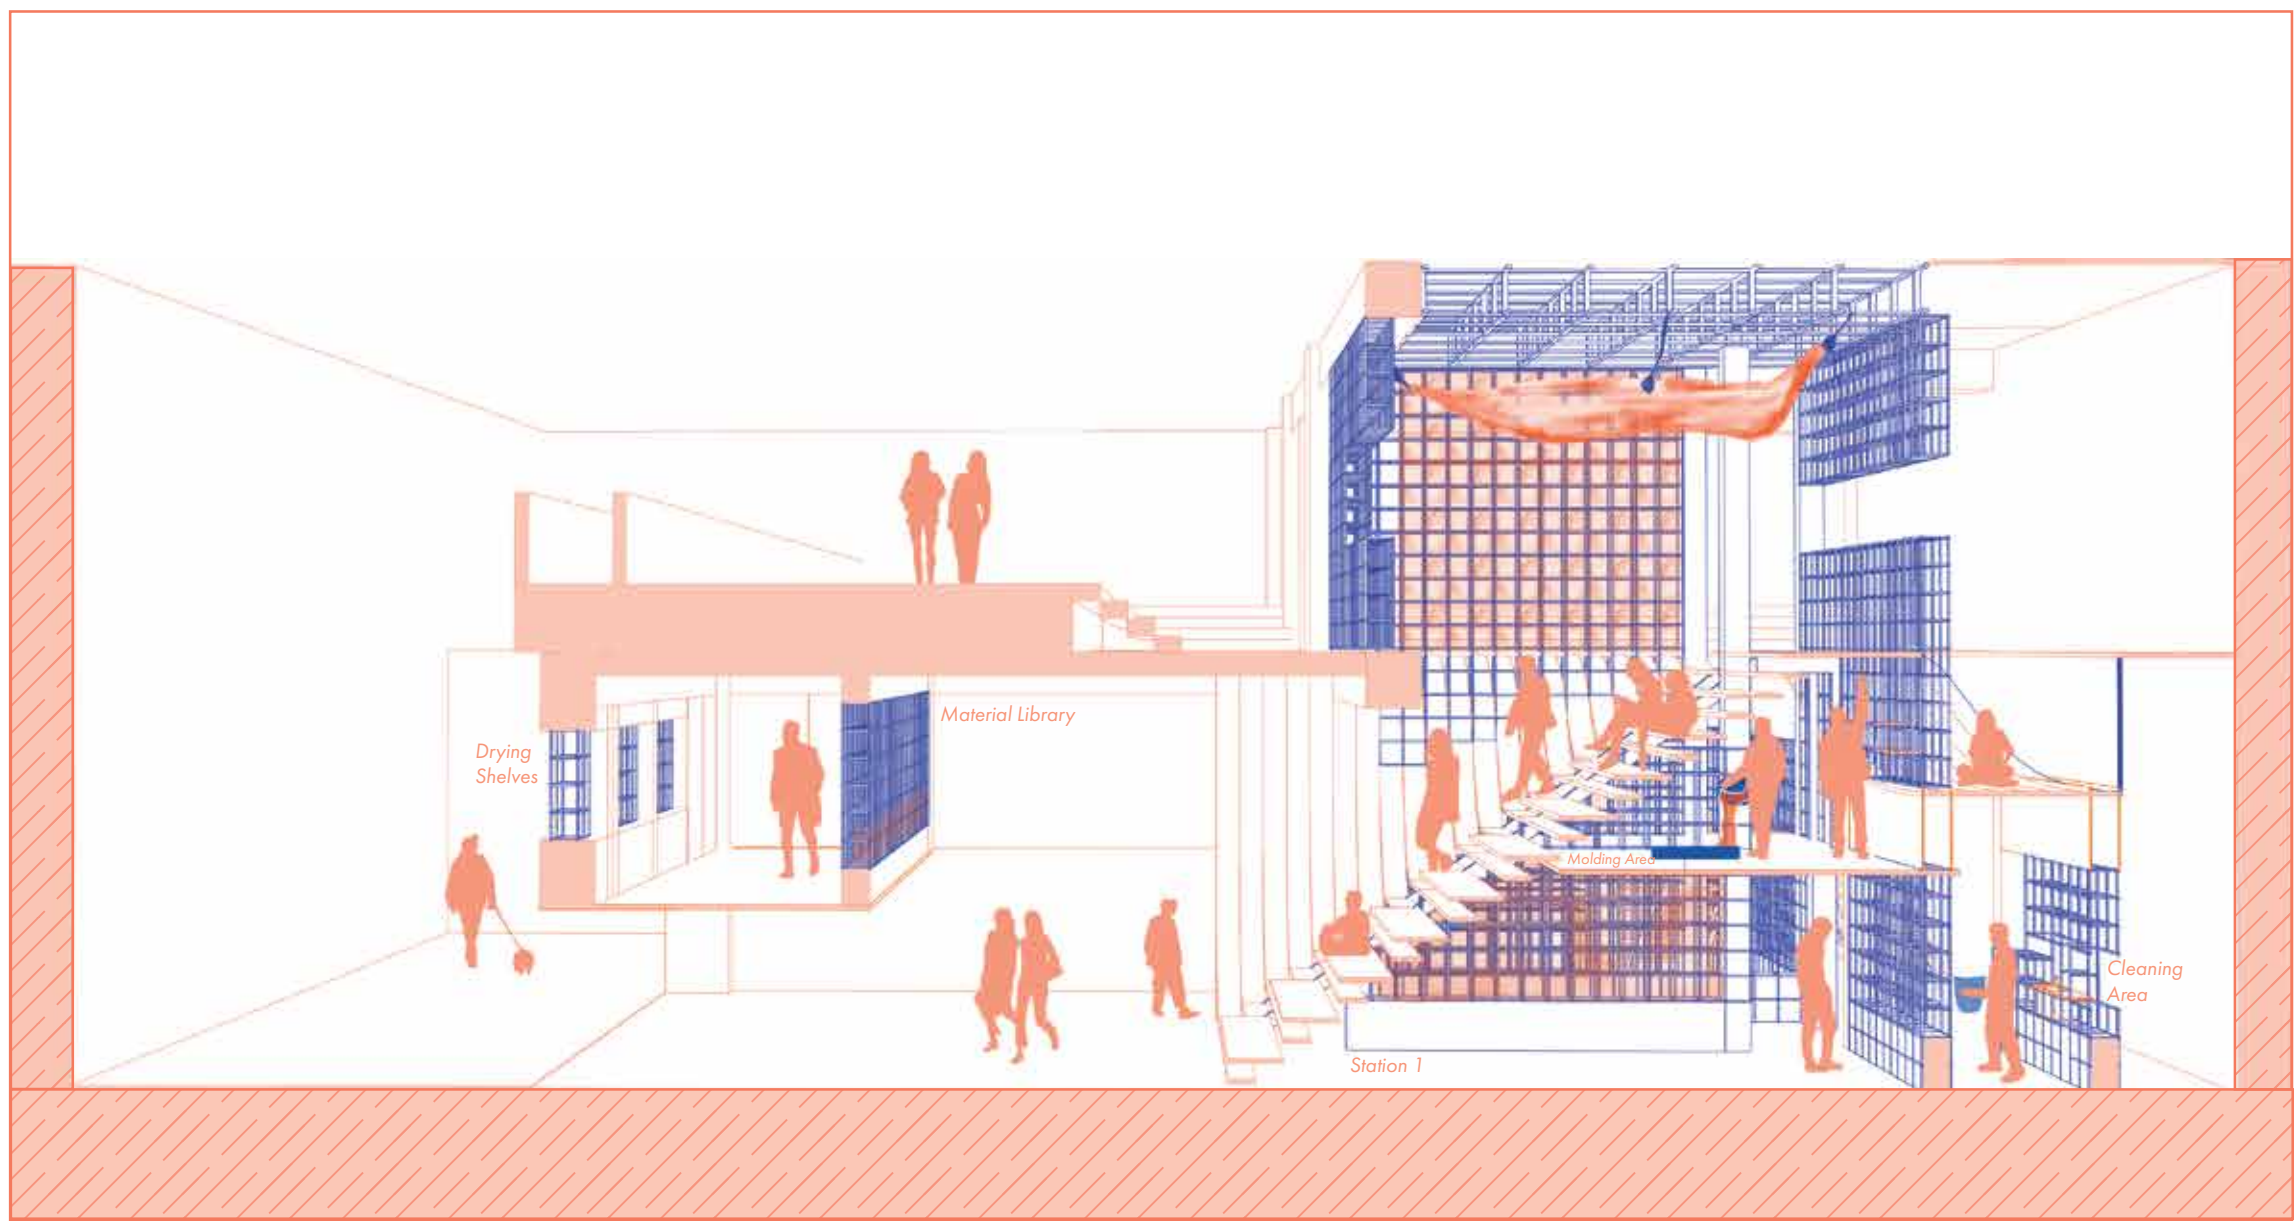
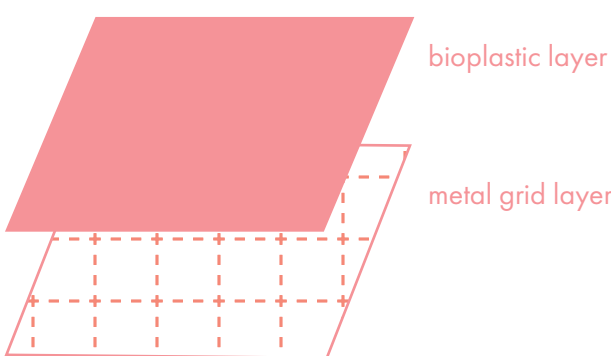


Perspective Section

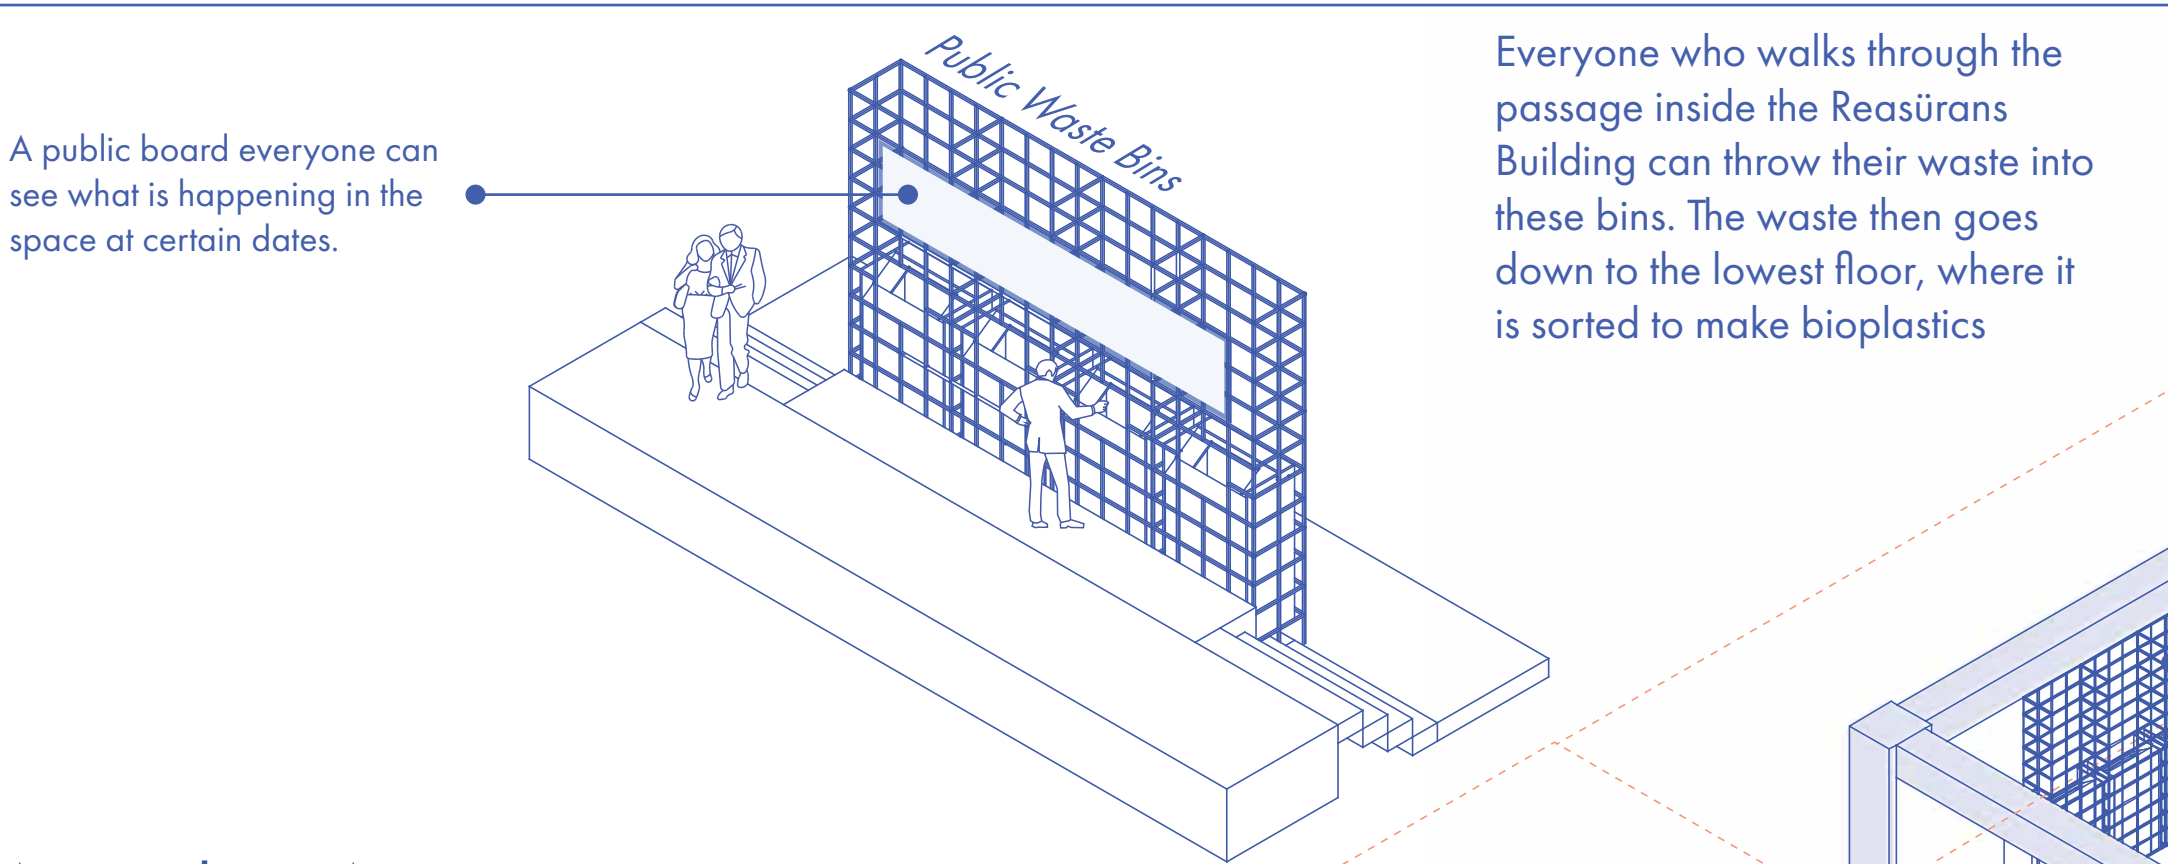


Accommodation Area


There is an accommodation area in the archive space that includes four separate rooms for researchers and also provides sleeping bags and pillows for temporary workers. The area also has a kitchen, a living space, toilets, and showers.

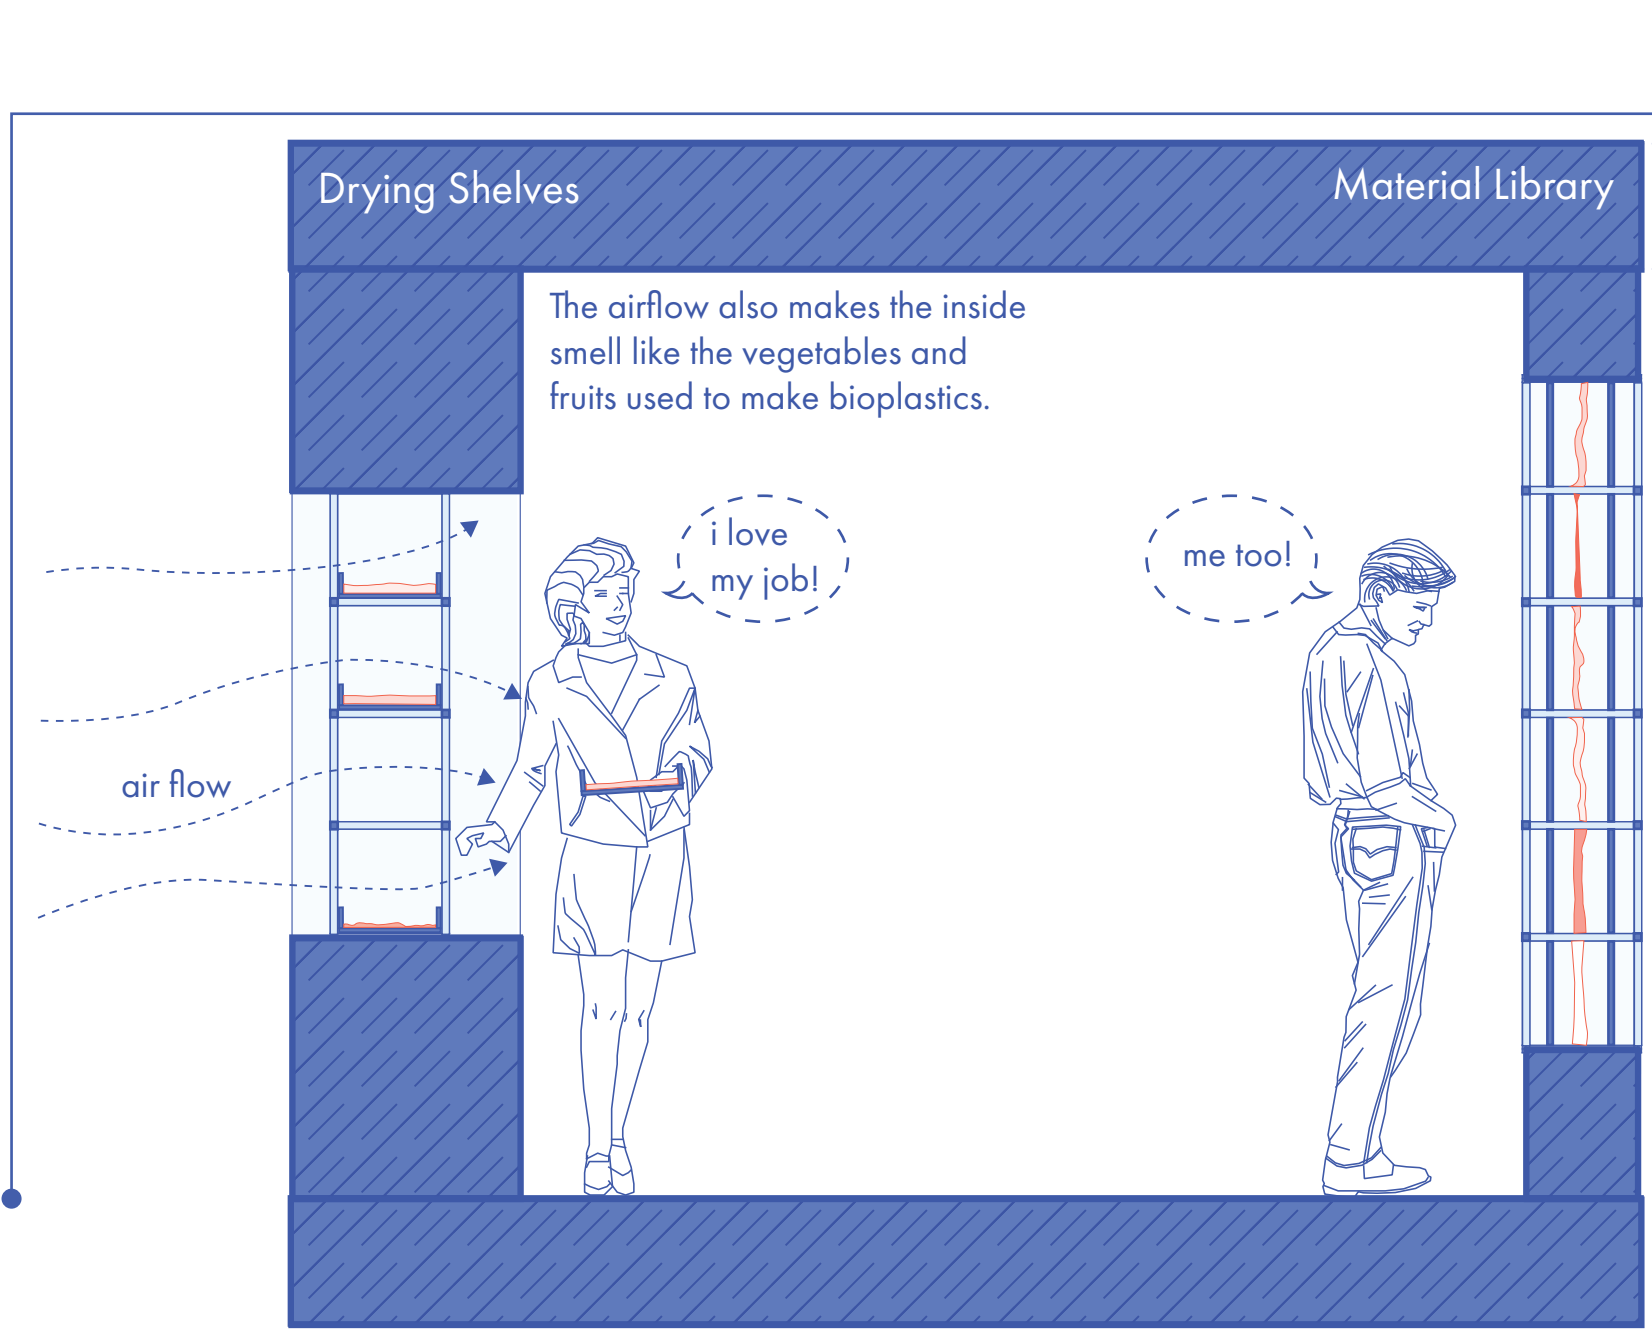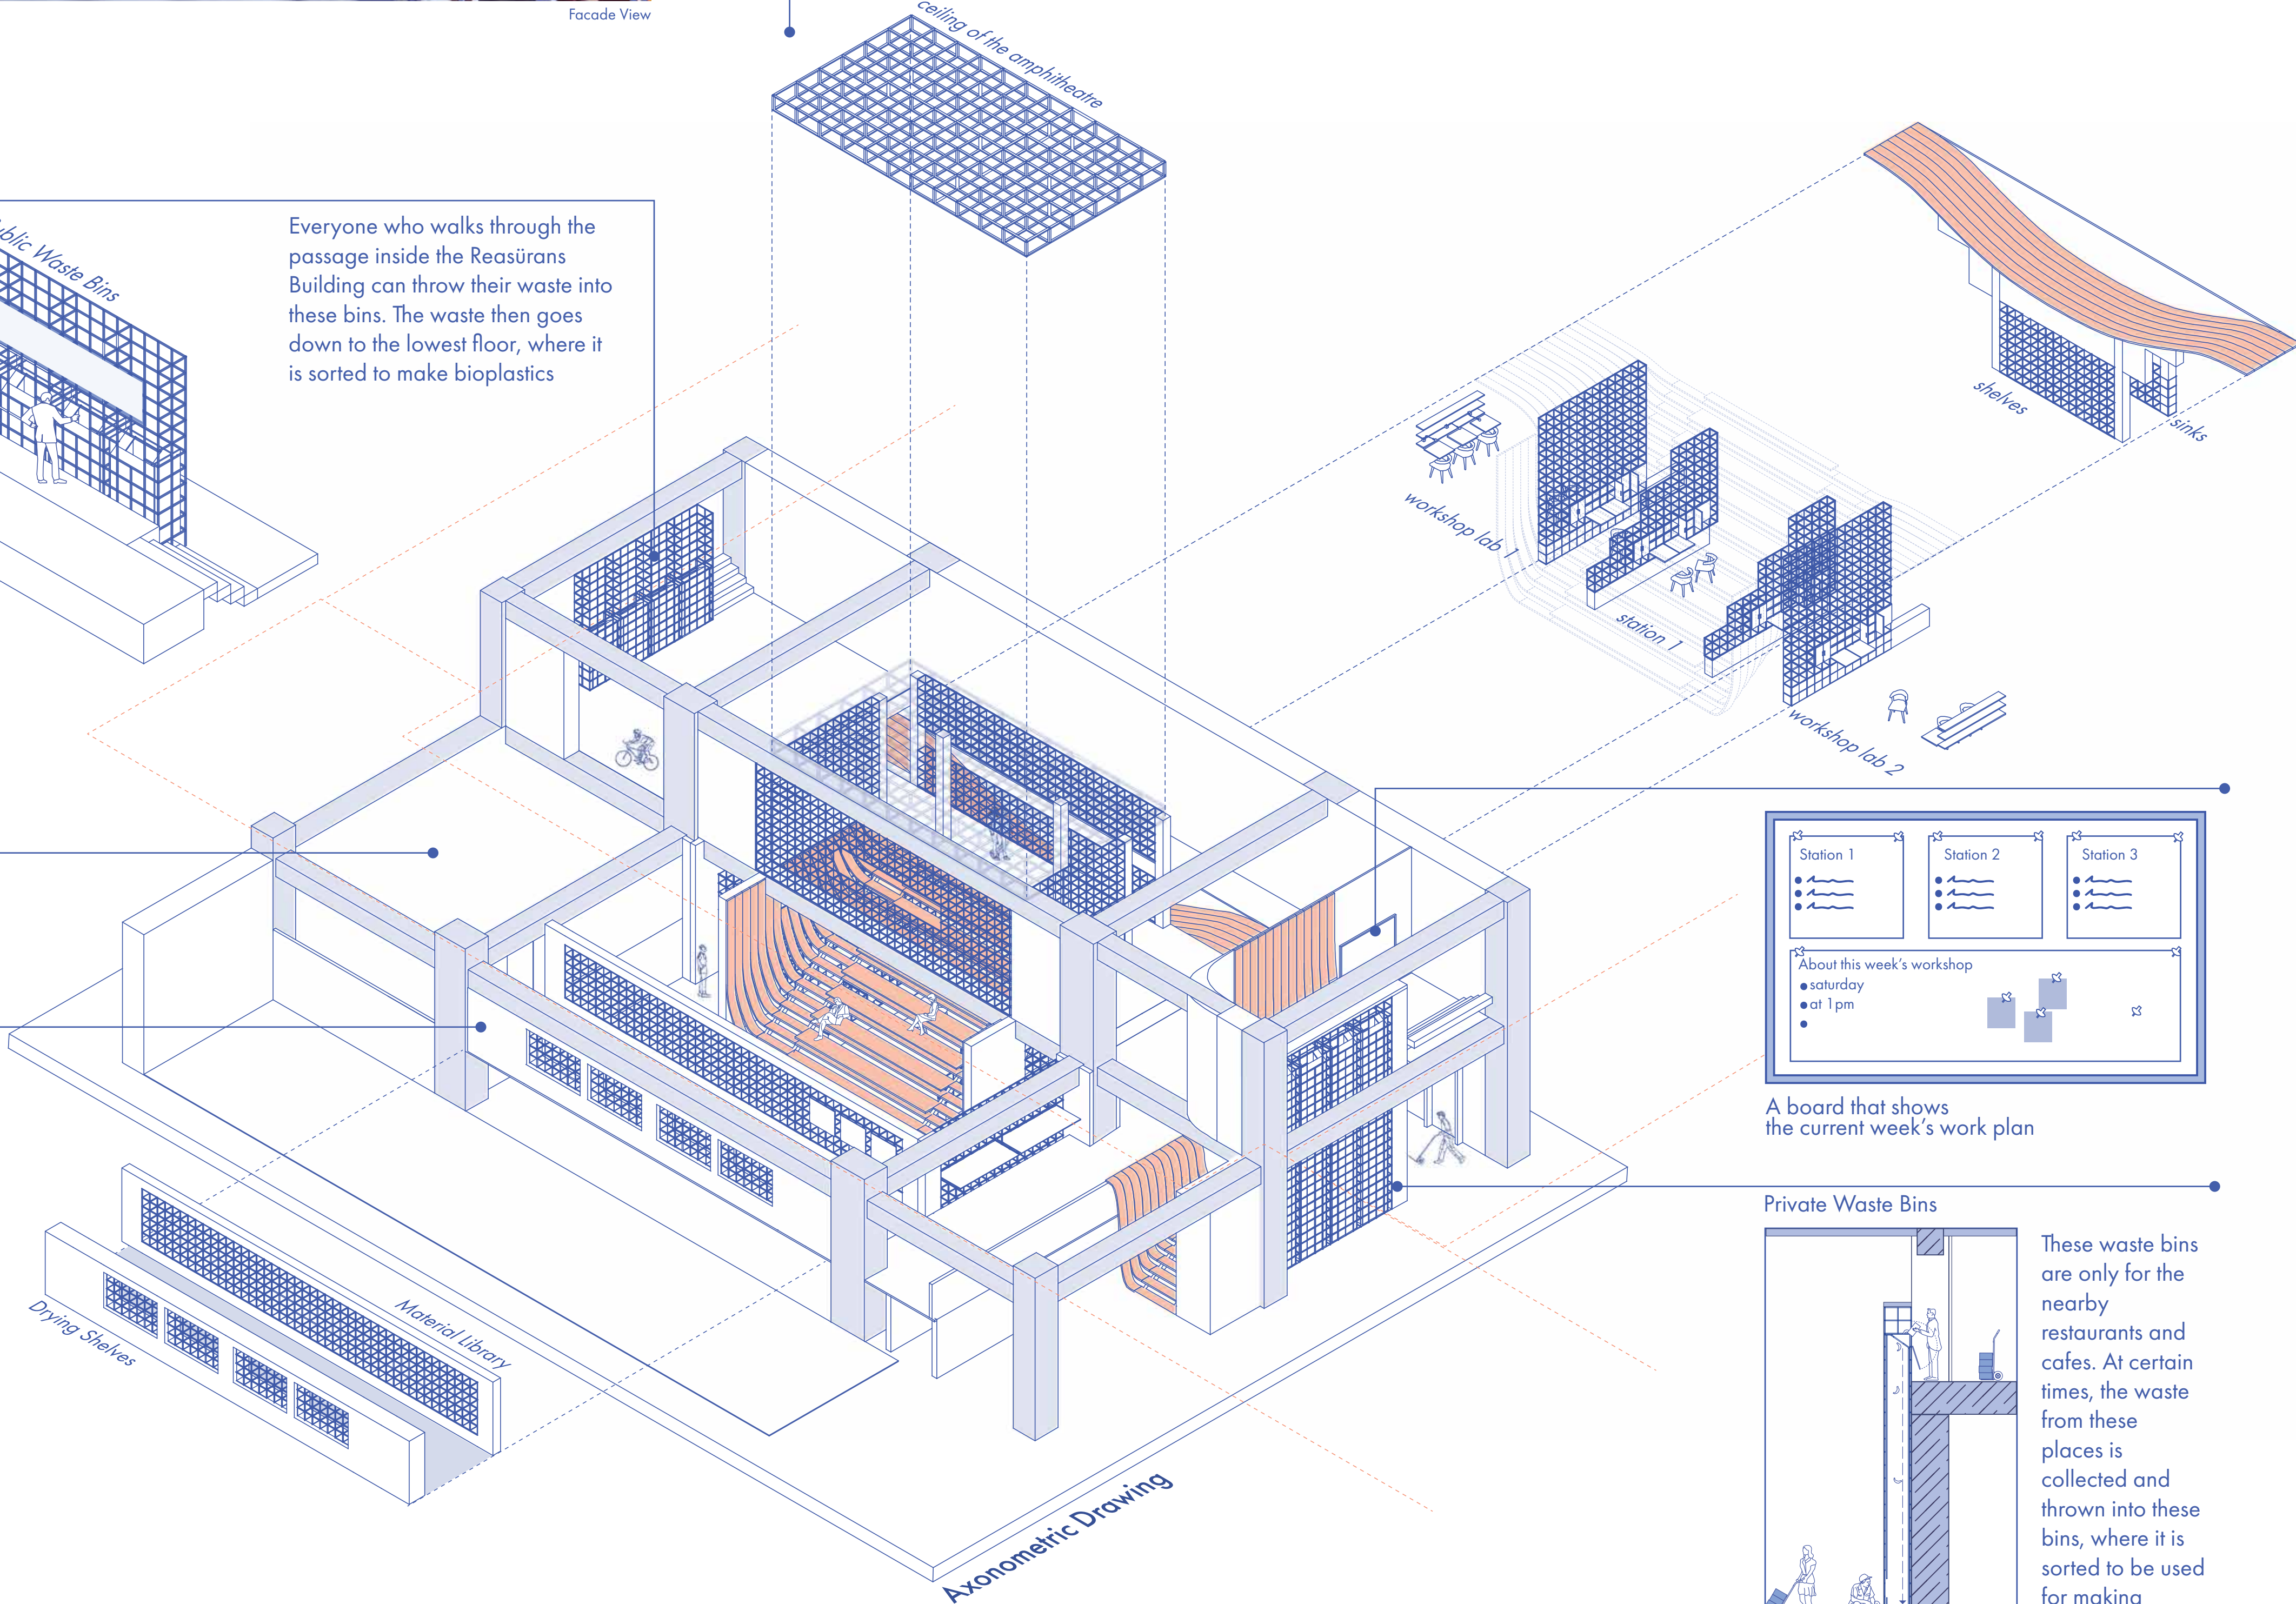

1/20 Section

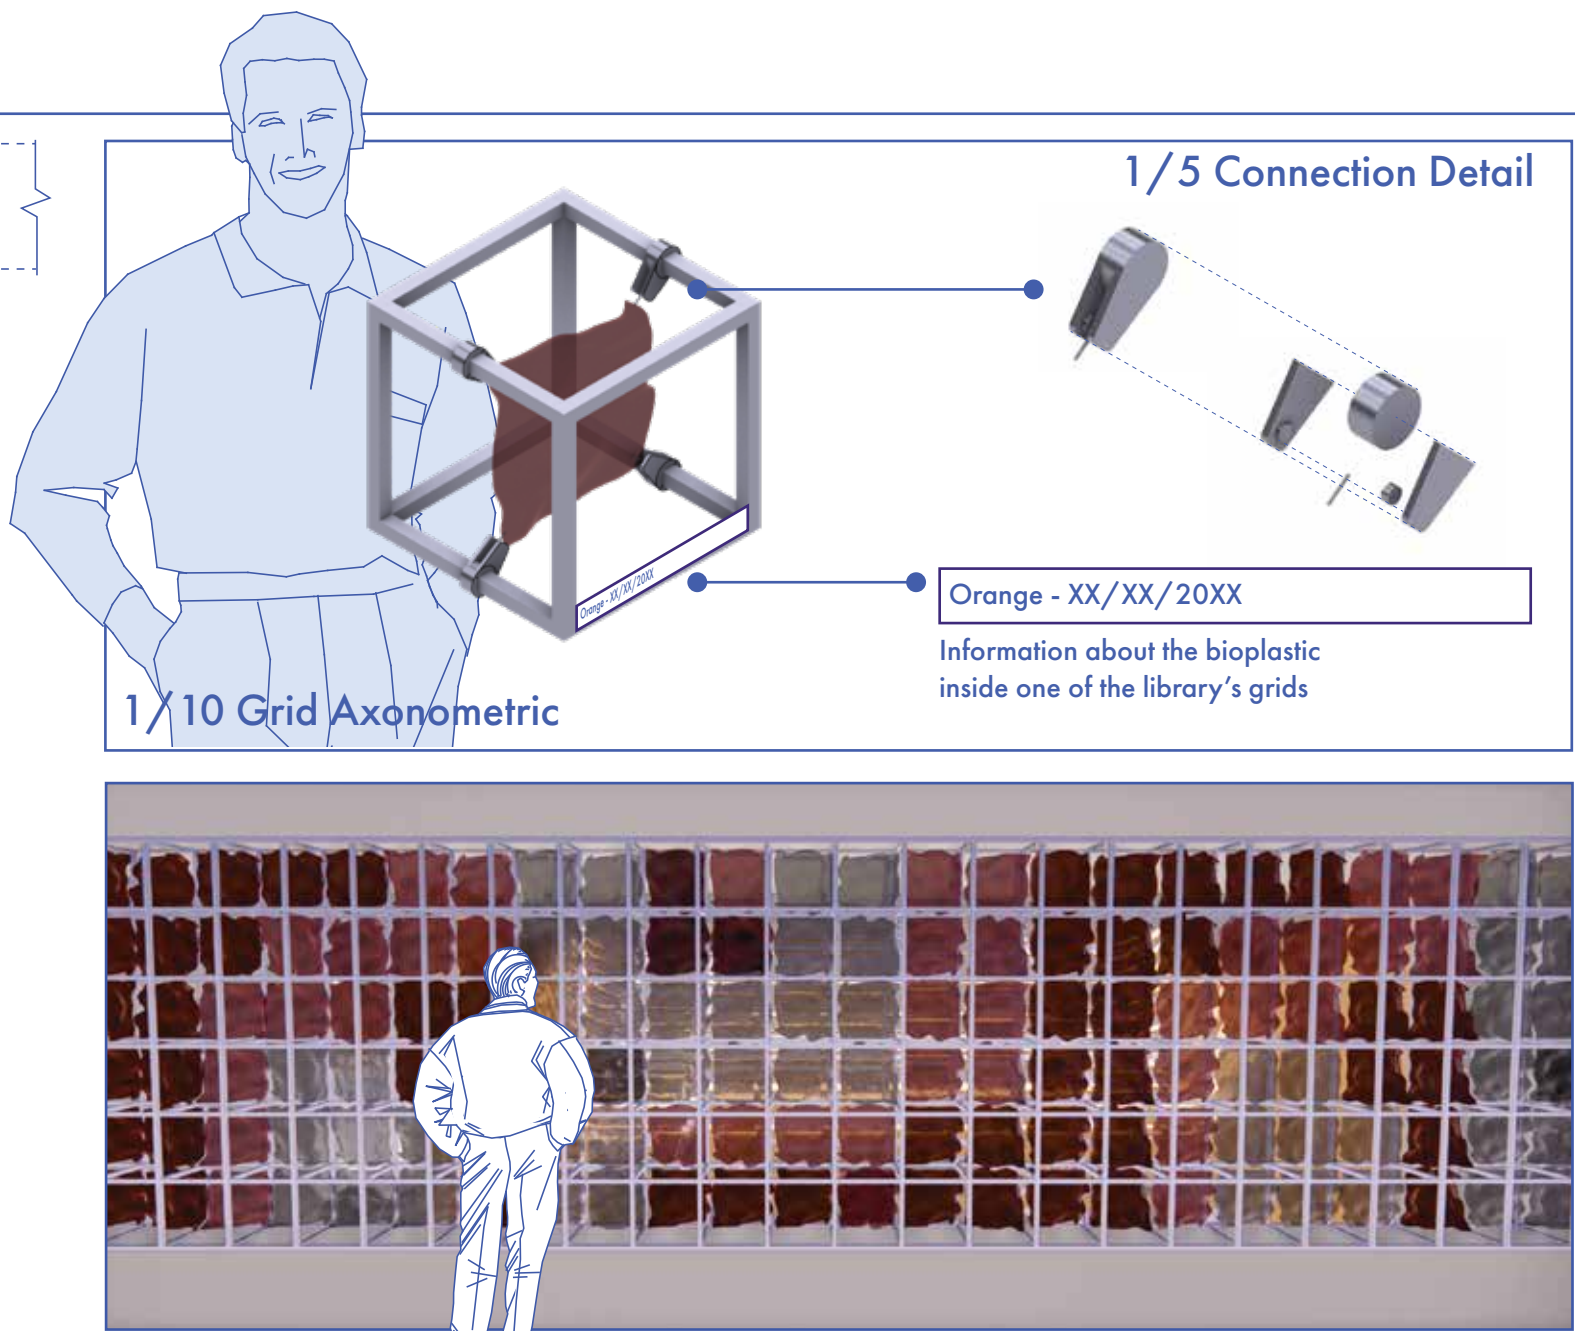

Private Waste Bins

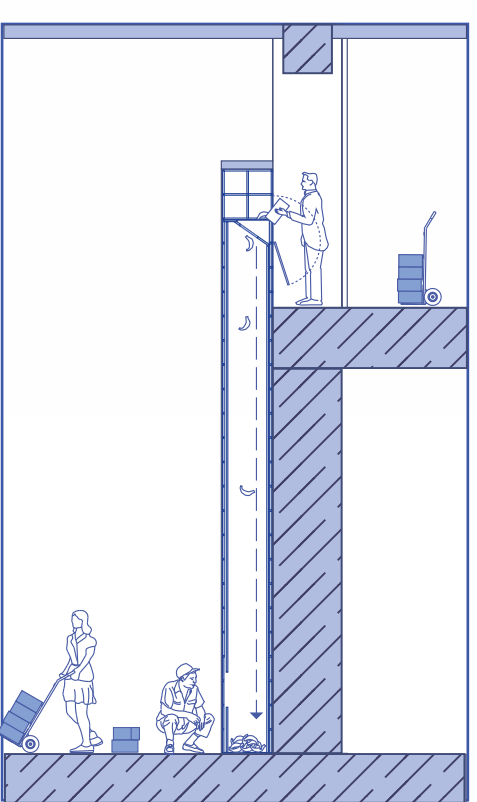

These waste bins are only for the nearby restaurants and cafes. At certain times, the waste from these places is collected and thrown into these bins, where it is sorted to be used for making bioplastic.